

MASSERIA LAMIOLA

Contrada Montalbano Ostuni (BR)



PLANIMETRIE – PROSPETTI – SEZIONI

00 - PLANIMETRIA DELLA MASSERIA E DELLE AREE ESTERNE CONNESSE

01 - Pianta Piano Terra

02 - Pianta Piano Primo



03 - Pianta Piano Copertura

04 – PROSPETTI

05 - SEZIONI


MASSERIA LAMIOLA
Contrada Montalbano
Ostuni (BR)
Gianfranco SCATIGNA
1990

PLANIMETRIA DELLA MASSERIA E DELLE
AREE ESTERNE CONNESSE

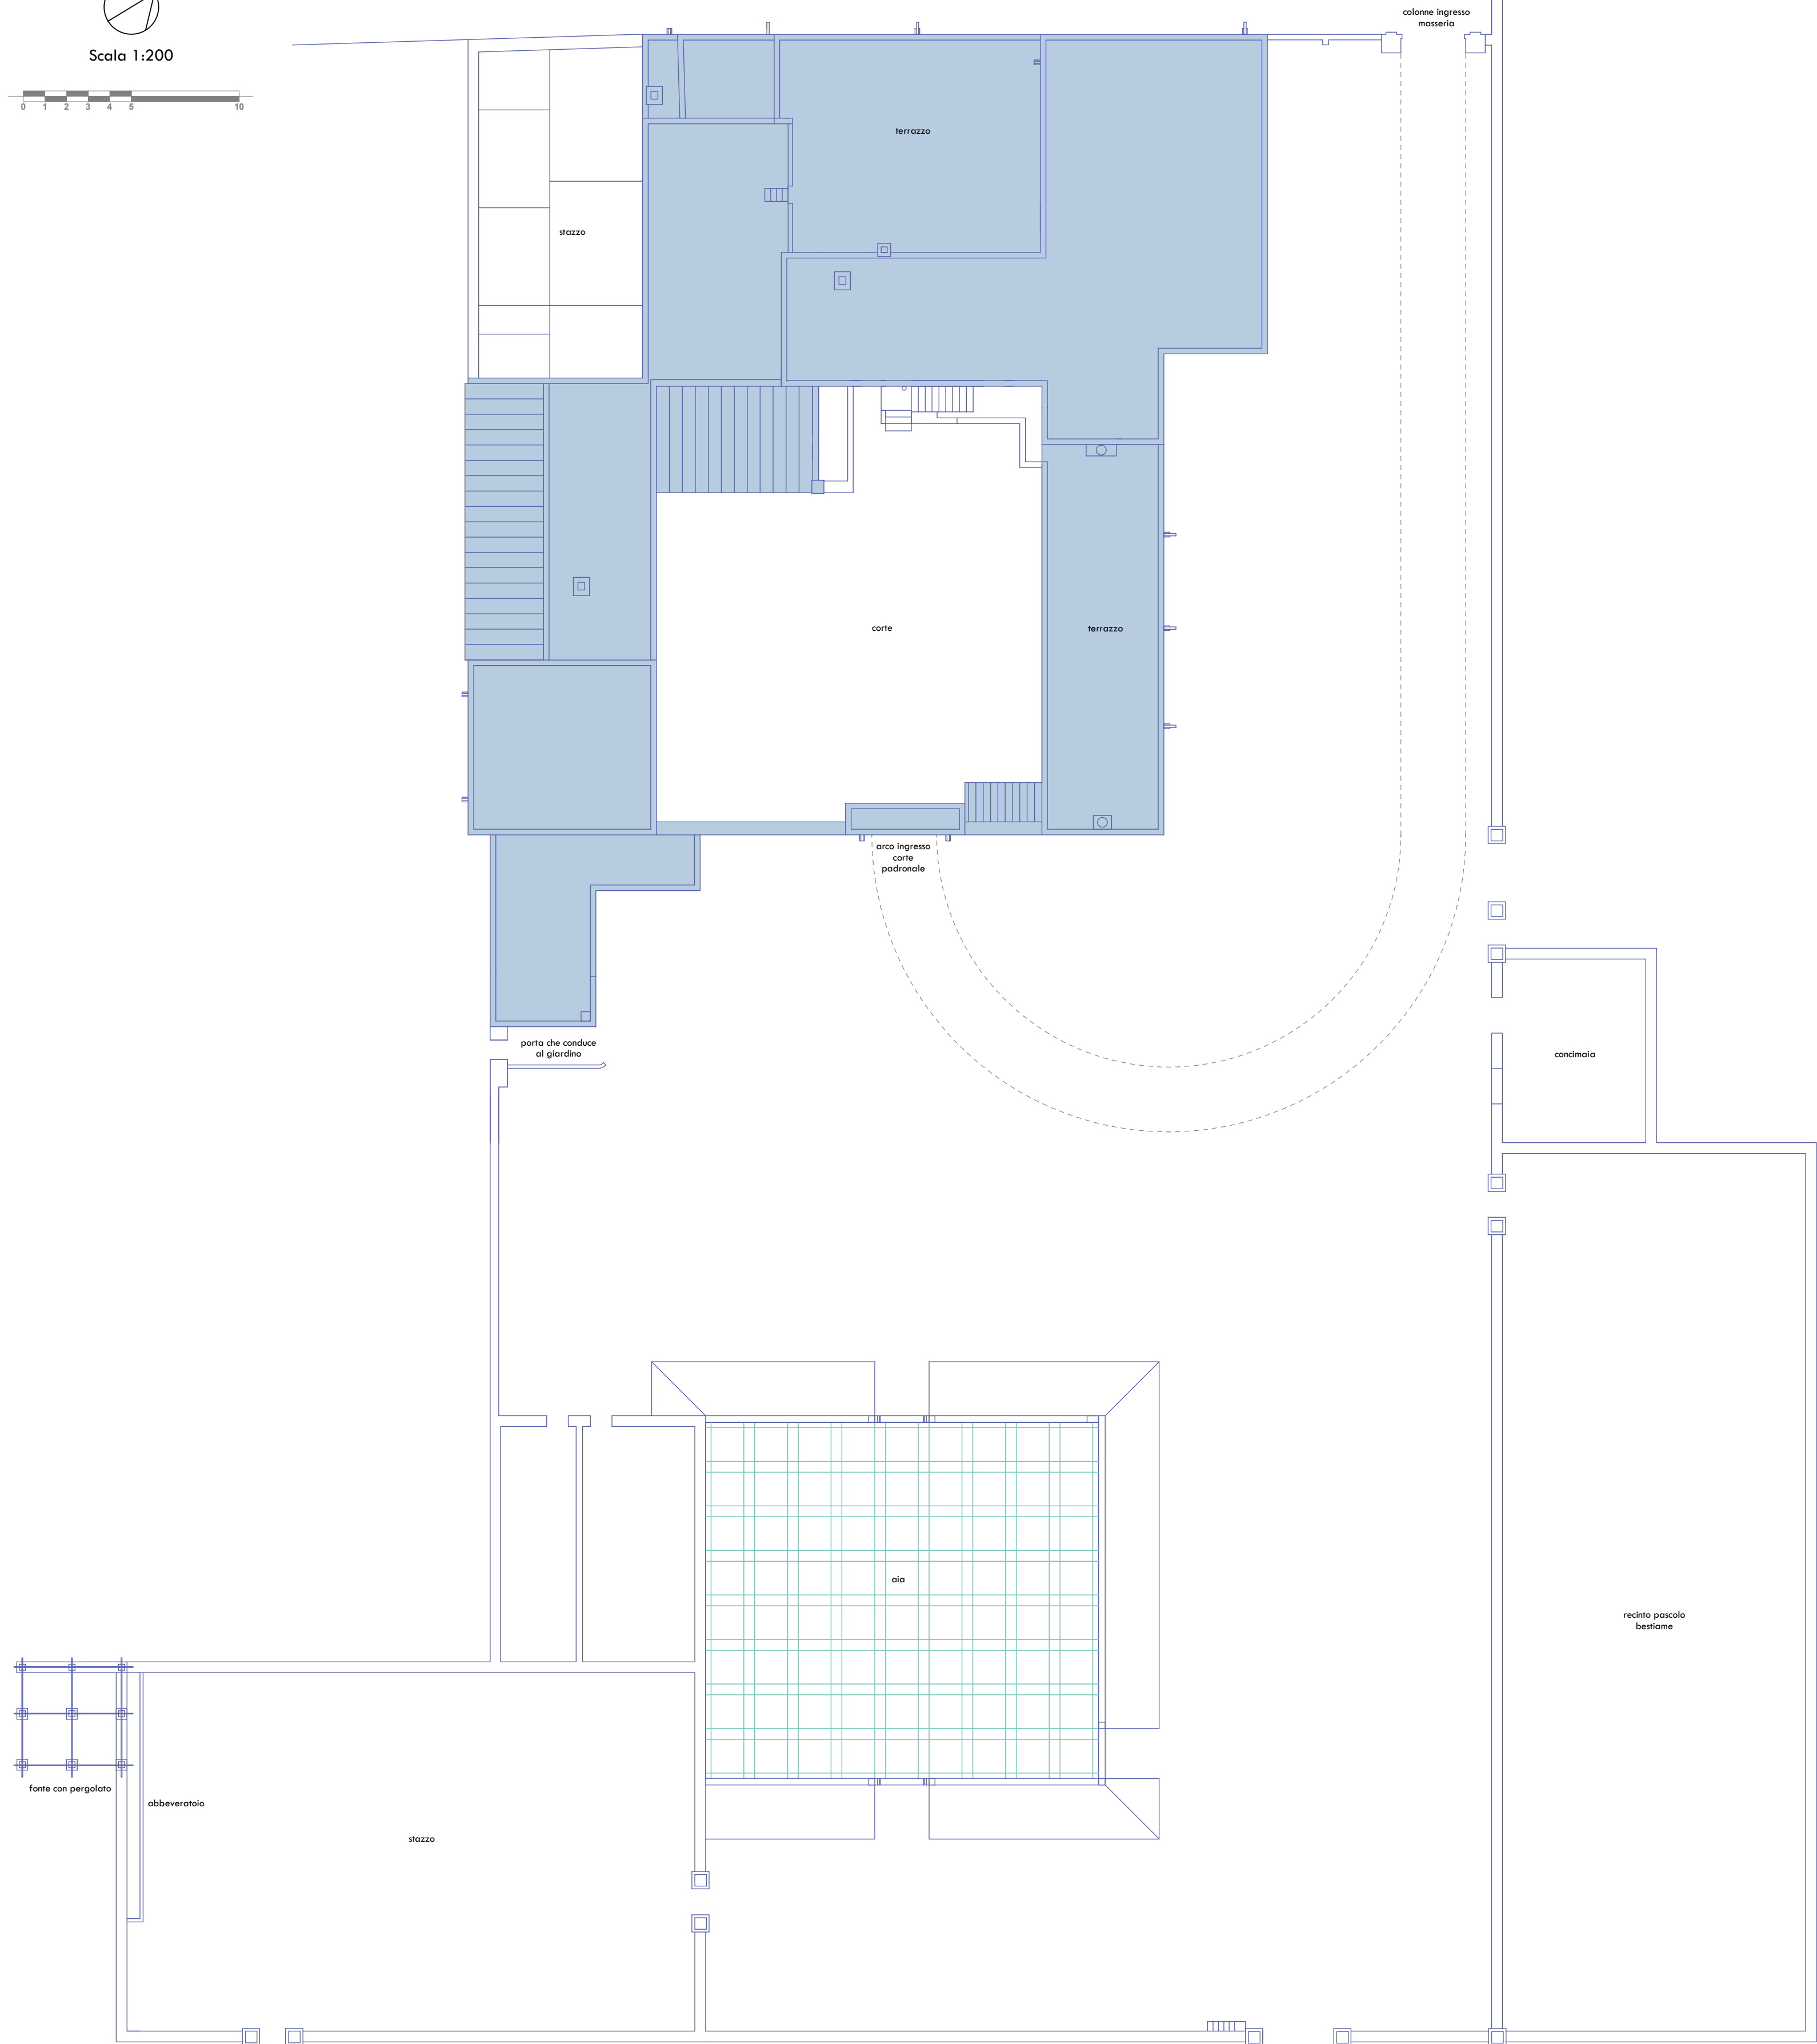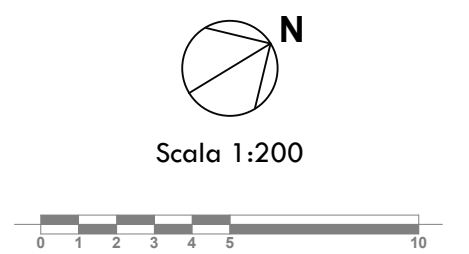

MASSERIA LAMIOLA
Contrada Montalbano
Ostuni (BR)


Gianfranco SCATIGNA
1990

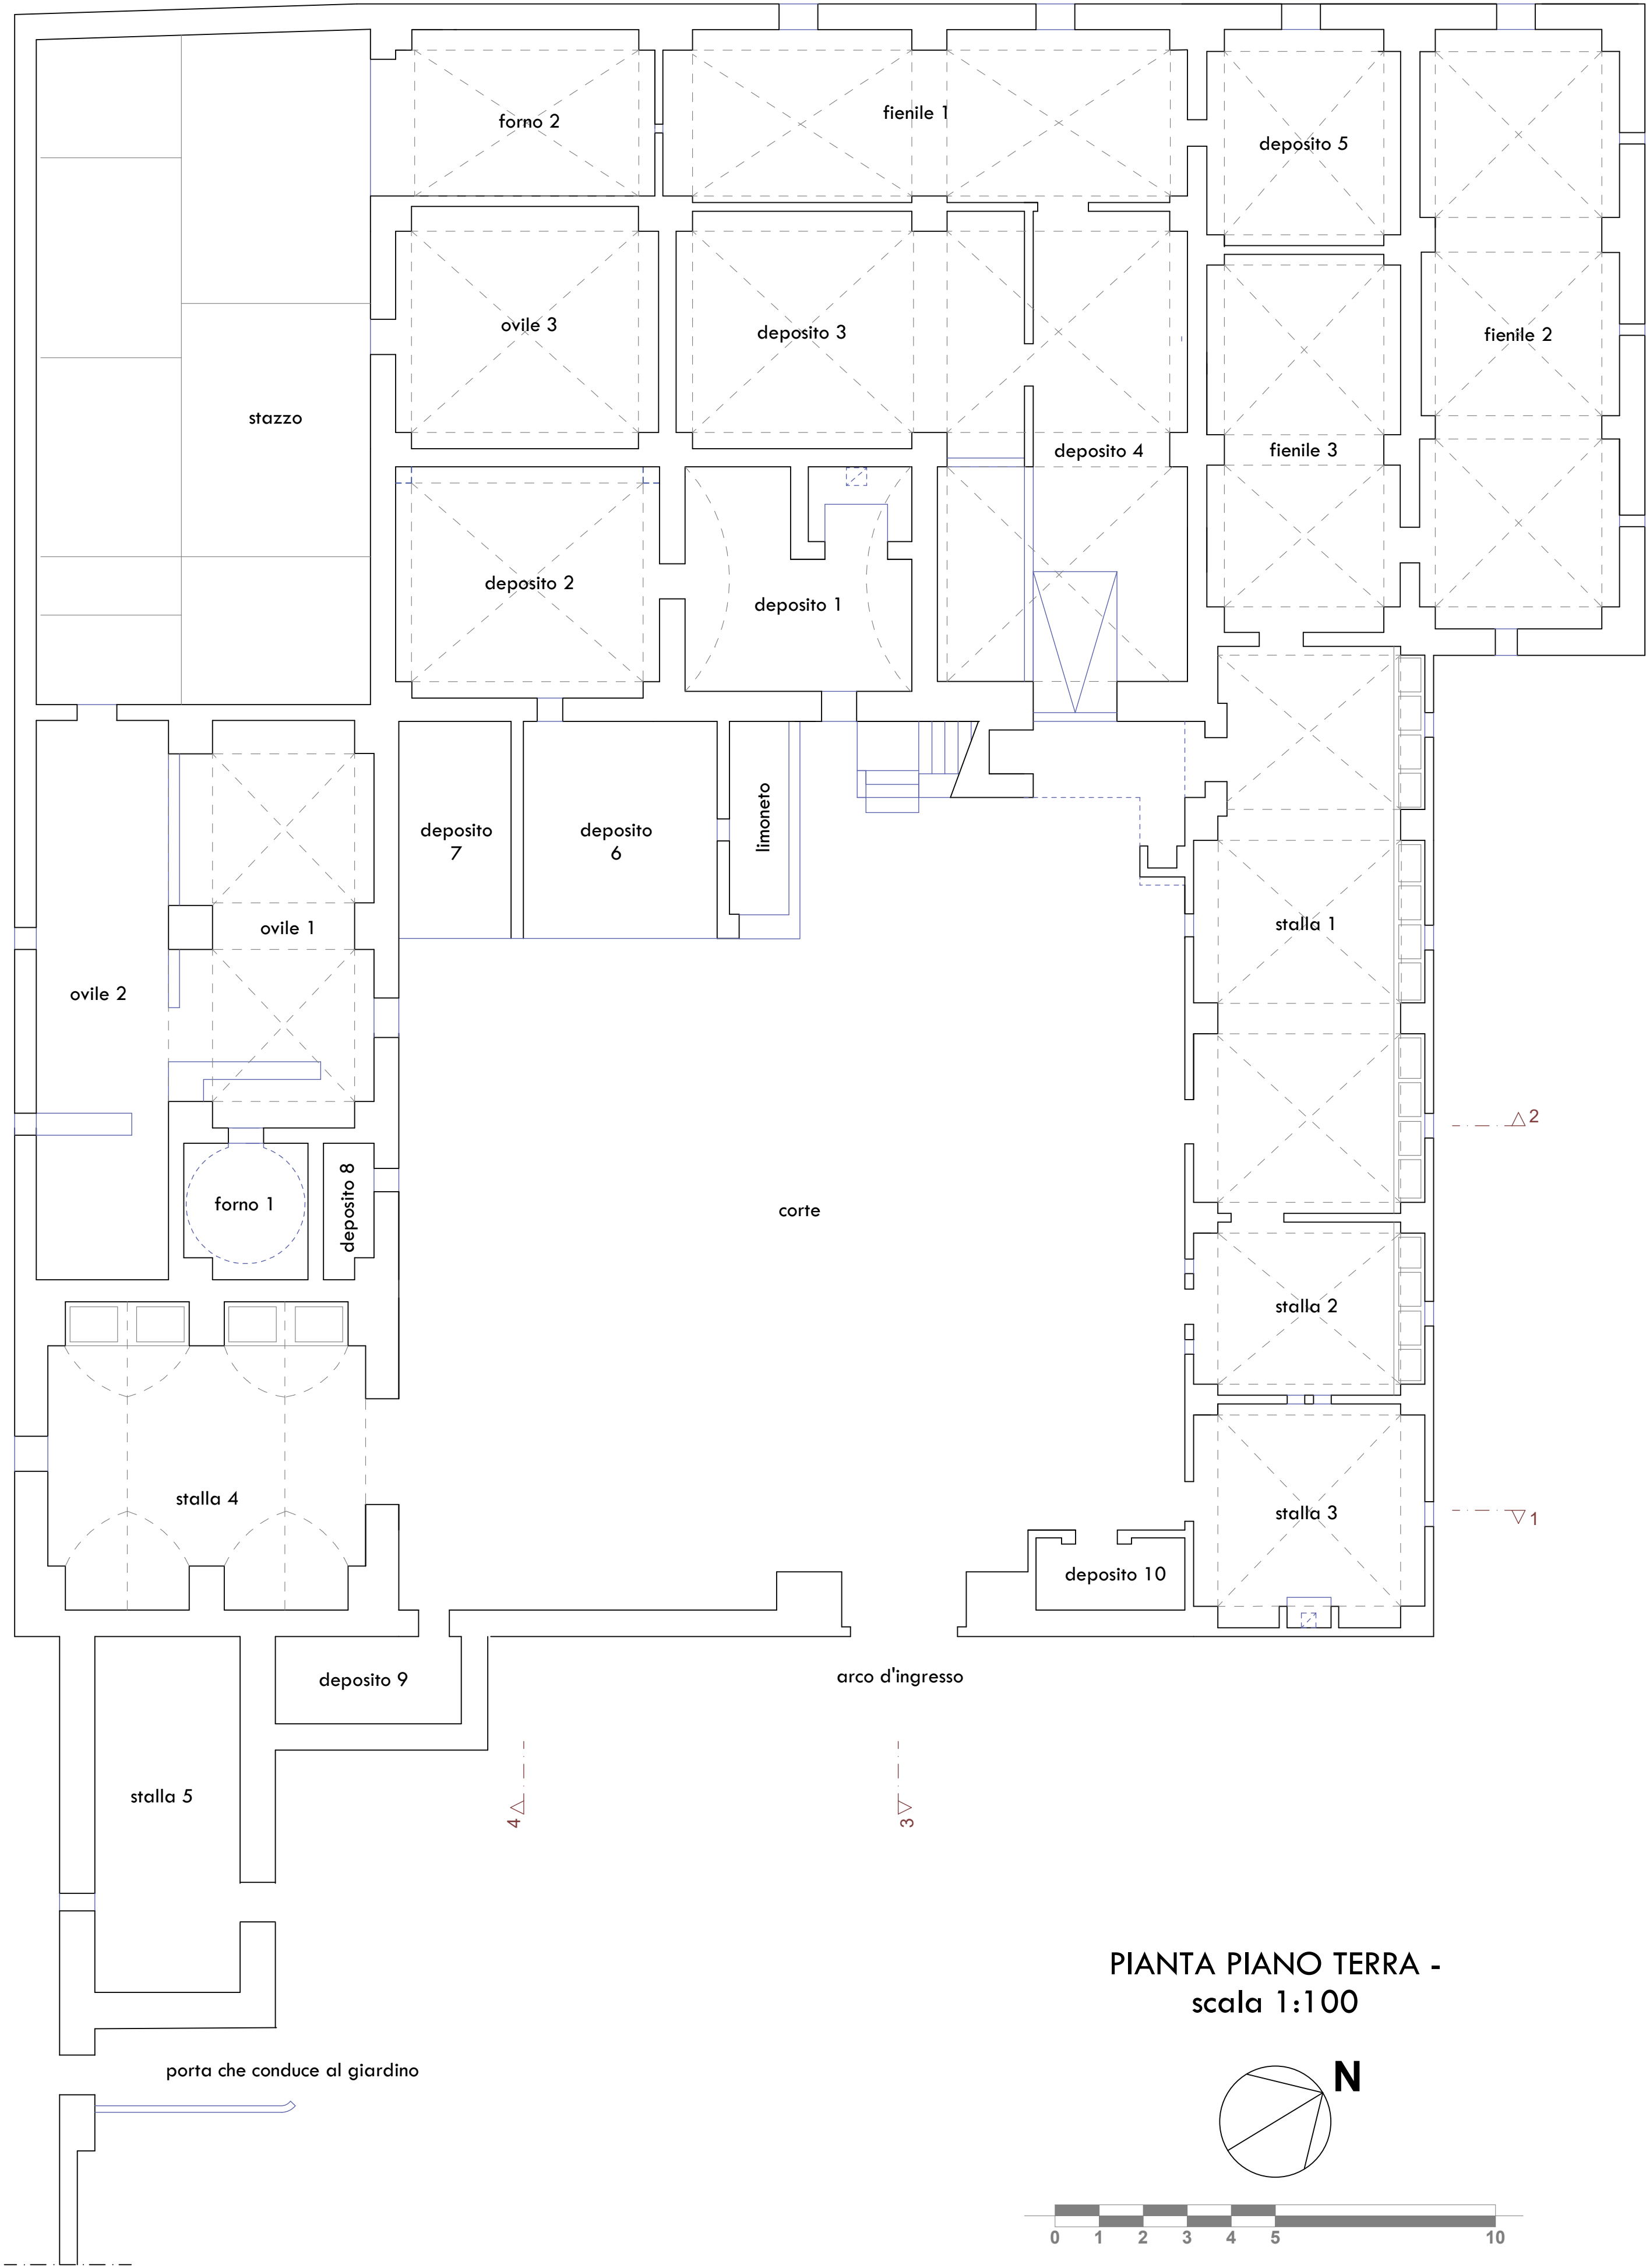


PIANTA PIANO TERRA -
scala 1:100




PIANTA PIANO PRIMO -
scala 1:200

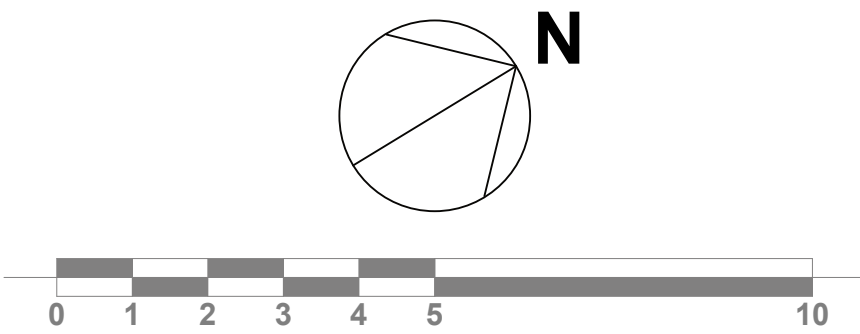

MASSERIA LAMIOLA
Contrada Montalbano
Ostuni (BR)
Gianfranco SCATIGNA
1990

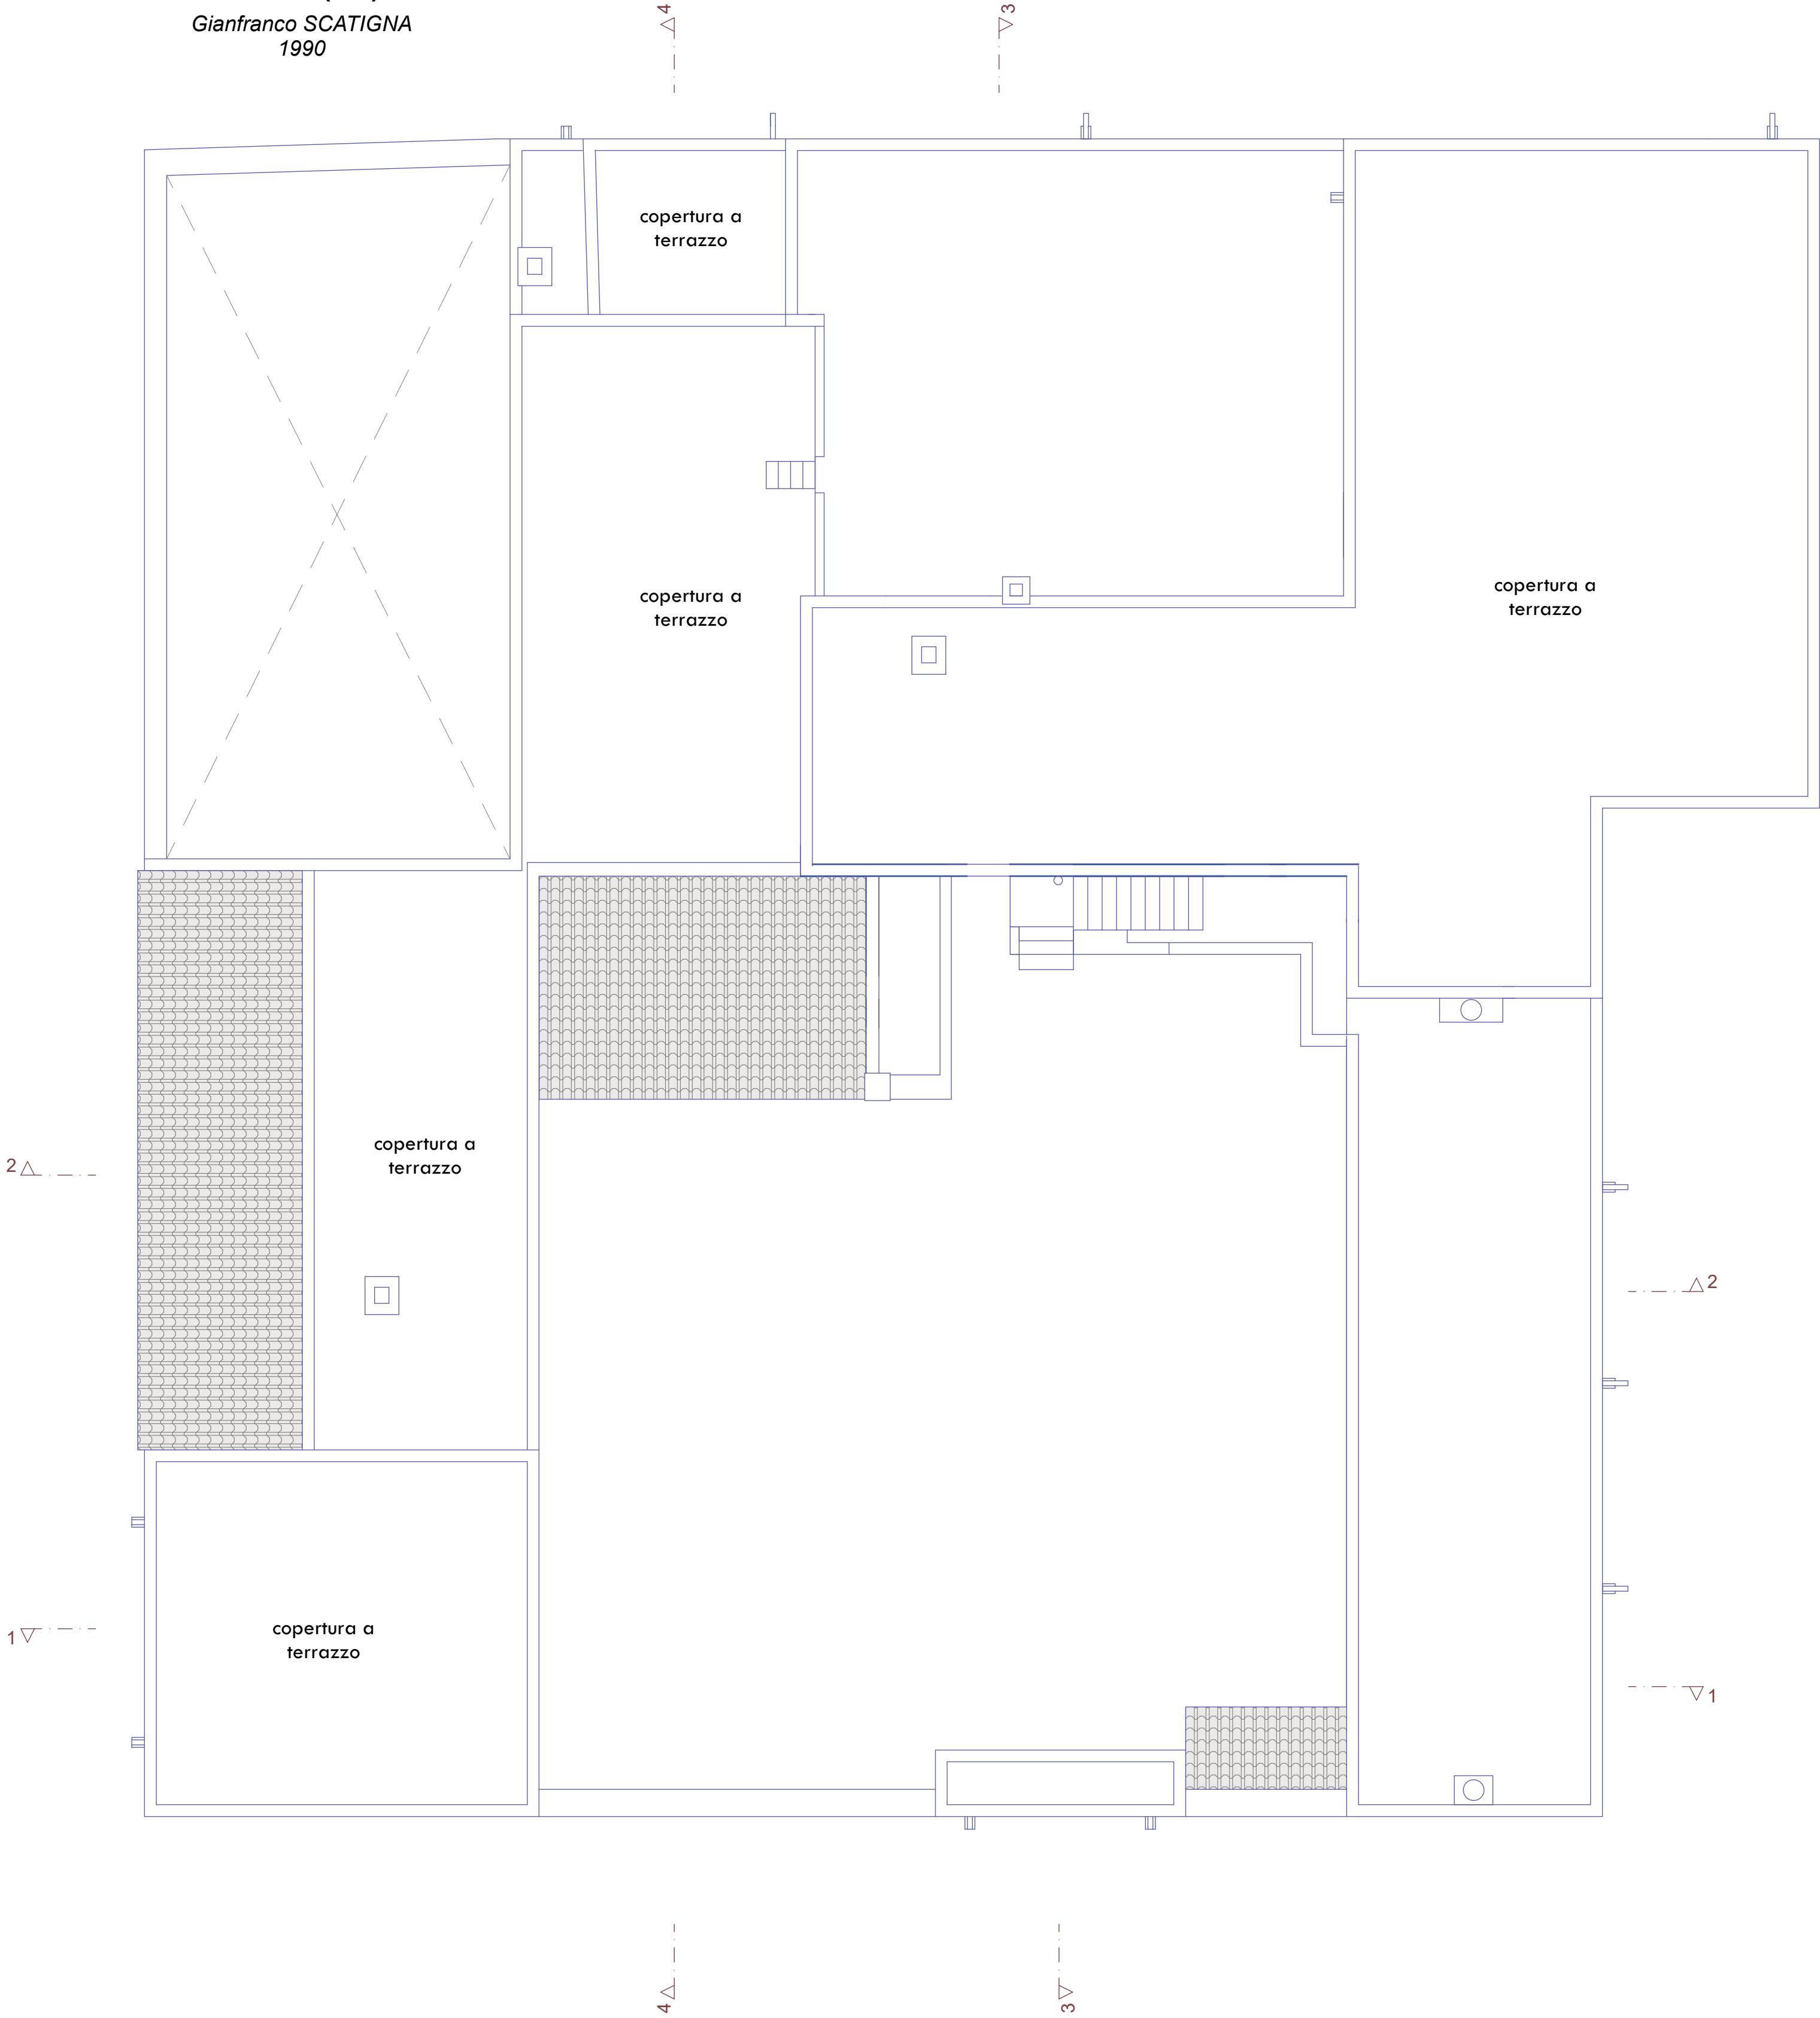


PIANTA COPERTURA-
scala 1:200

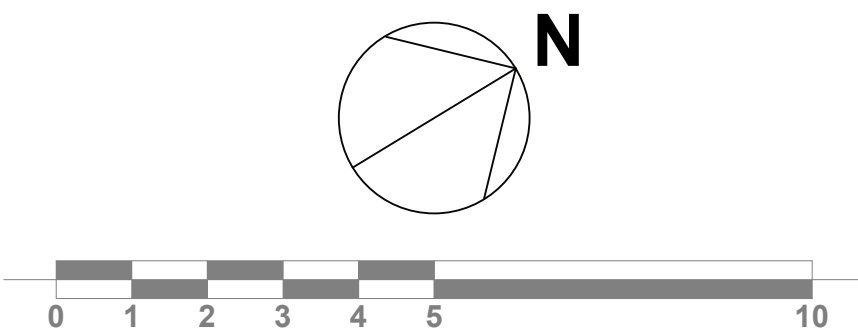


MASSERIA LAMIOLA
Contrada Montalbano
Ostuni (BR)


Gianfranco SCATIGNA
1990

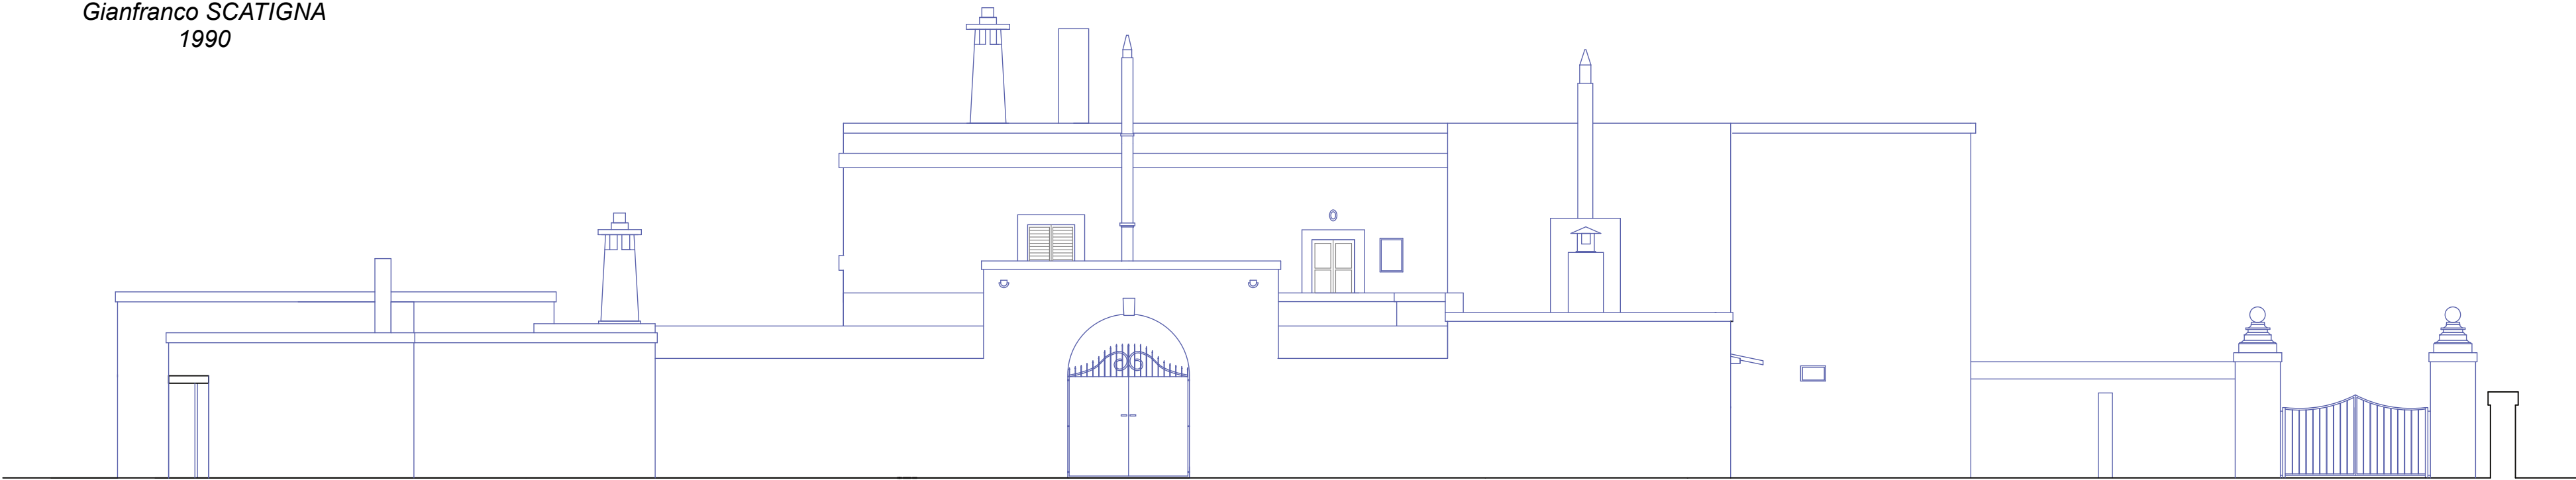


PROSPETTO ARCO D'INGRESSO CORTE -
Scala 1:100

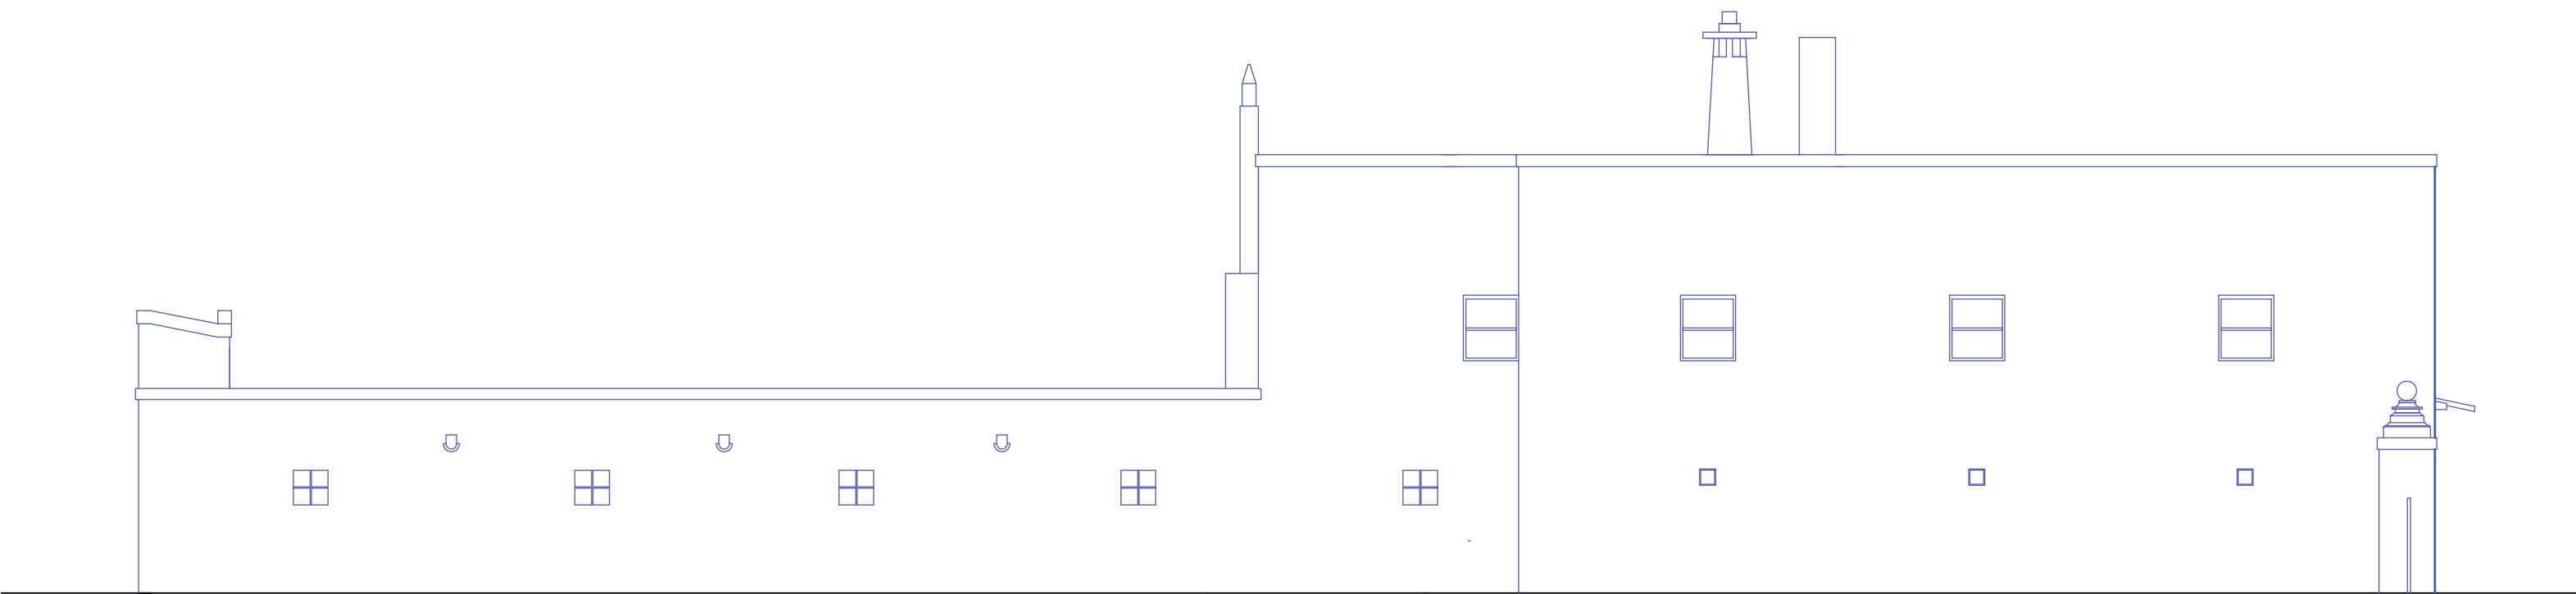

PROSPETTO SUL VIALE DI ACCESSO
- Scala 1:100

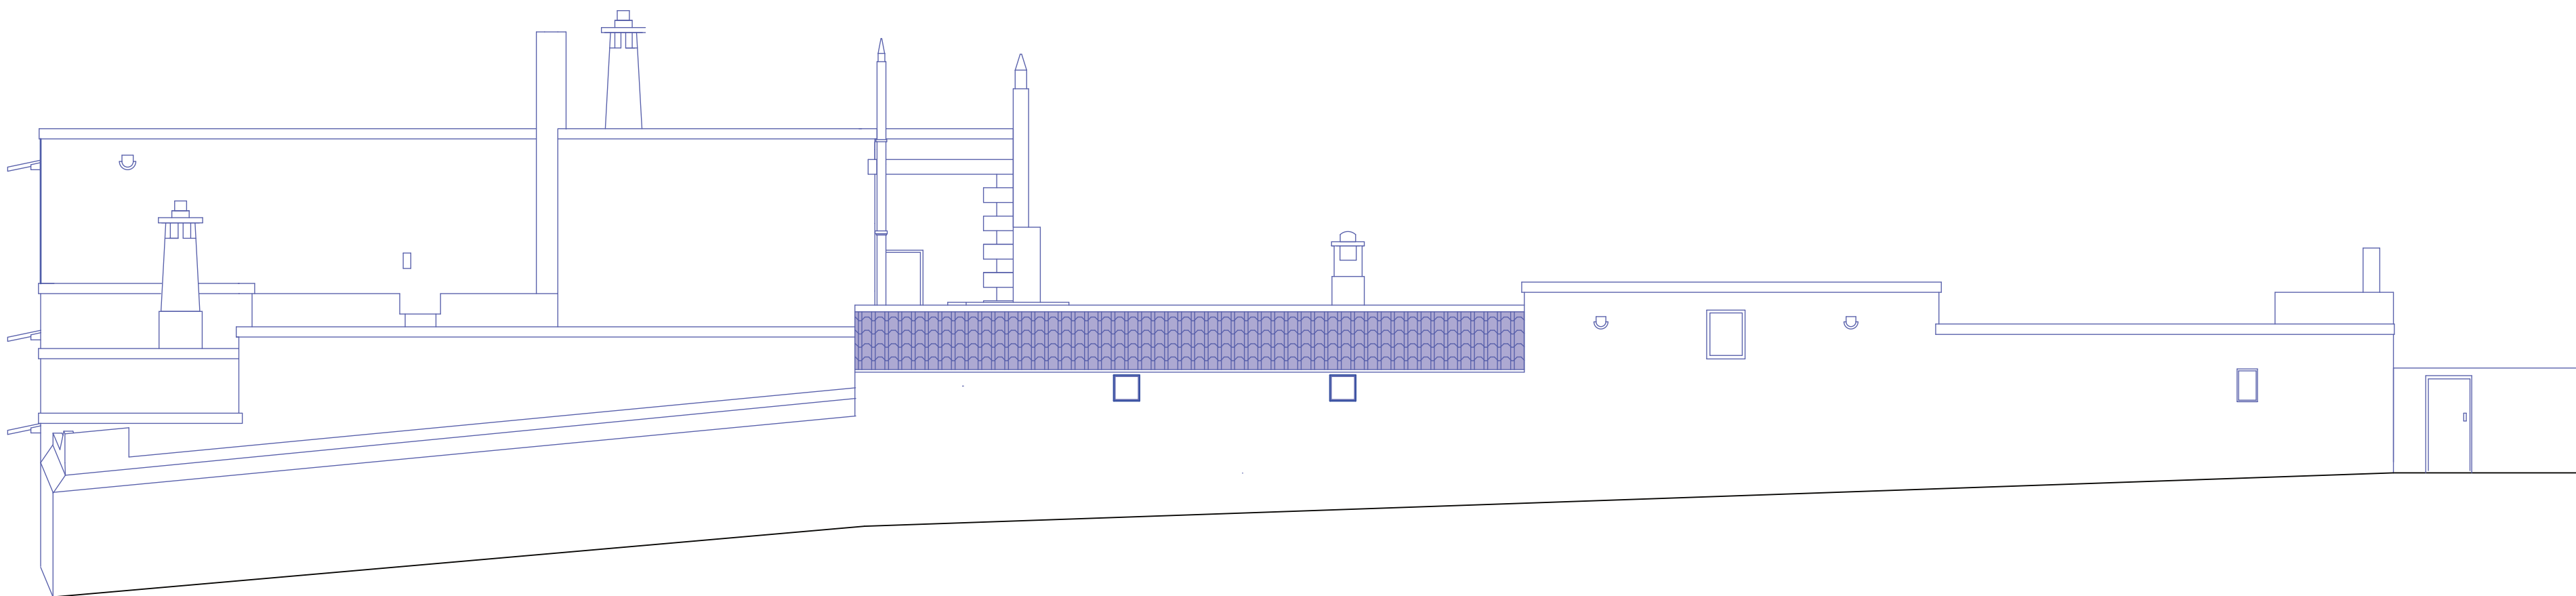


PROSPETTO SUL GIARDINO -
Scala 1:100

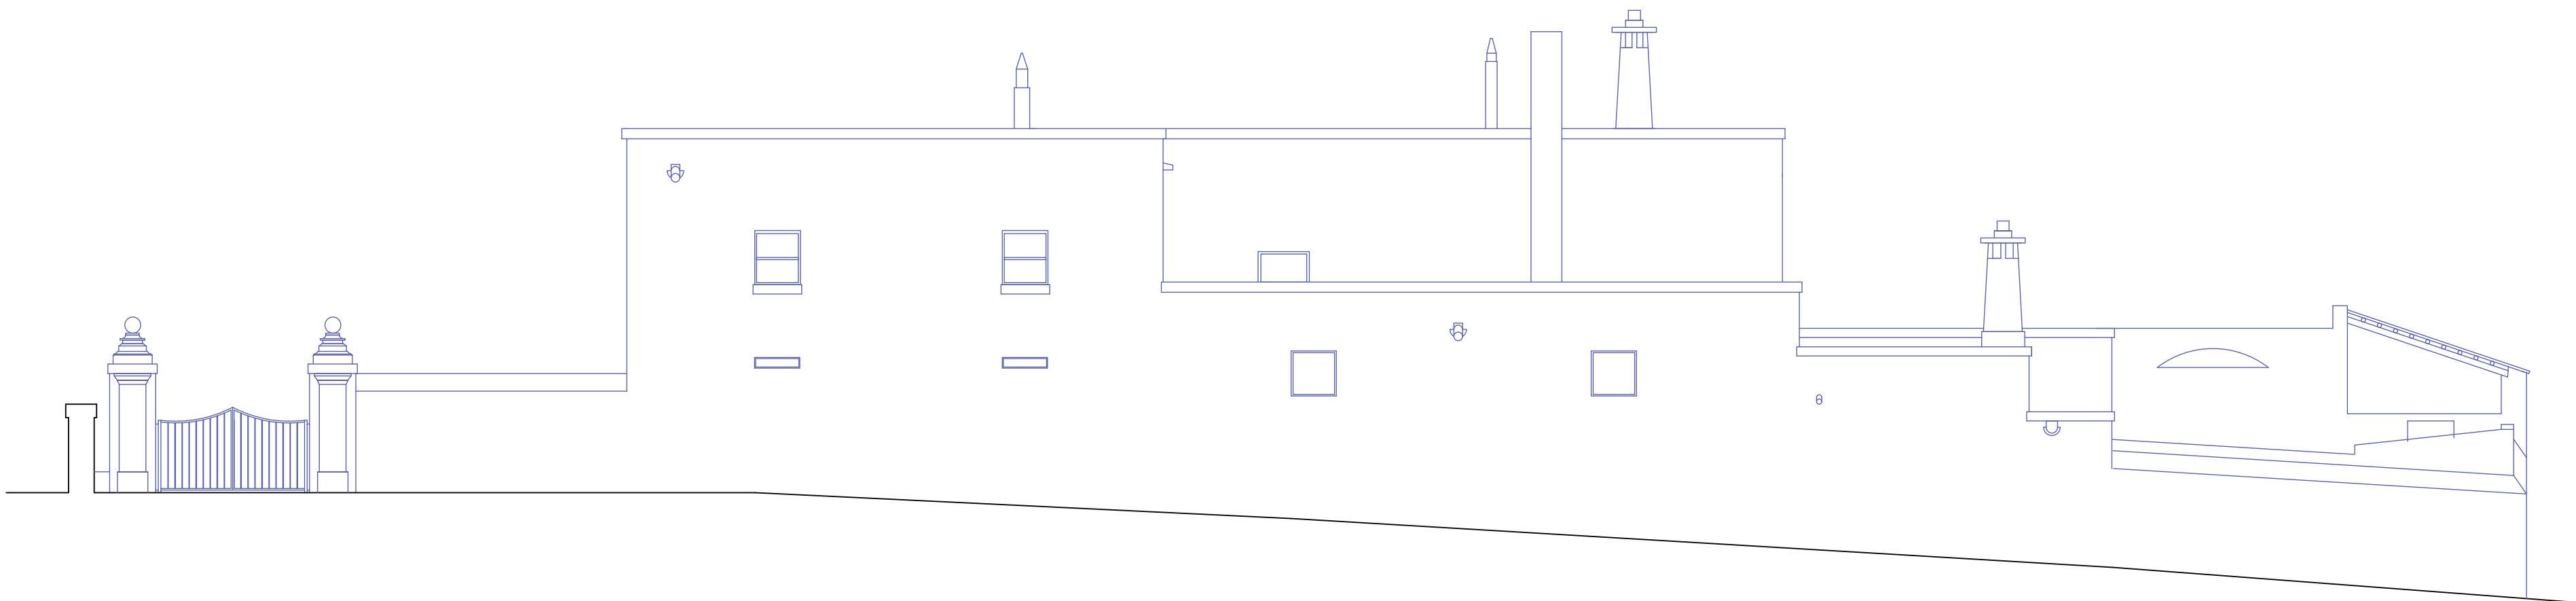


PROSPETTO SU VIA ASPROMONTE -
Scala 1:100




MASSERIA LAMIOLA
Contrada Montalbano
Ostuni (BR)
Gianfranco SCATIGNA
1990

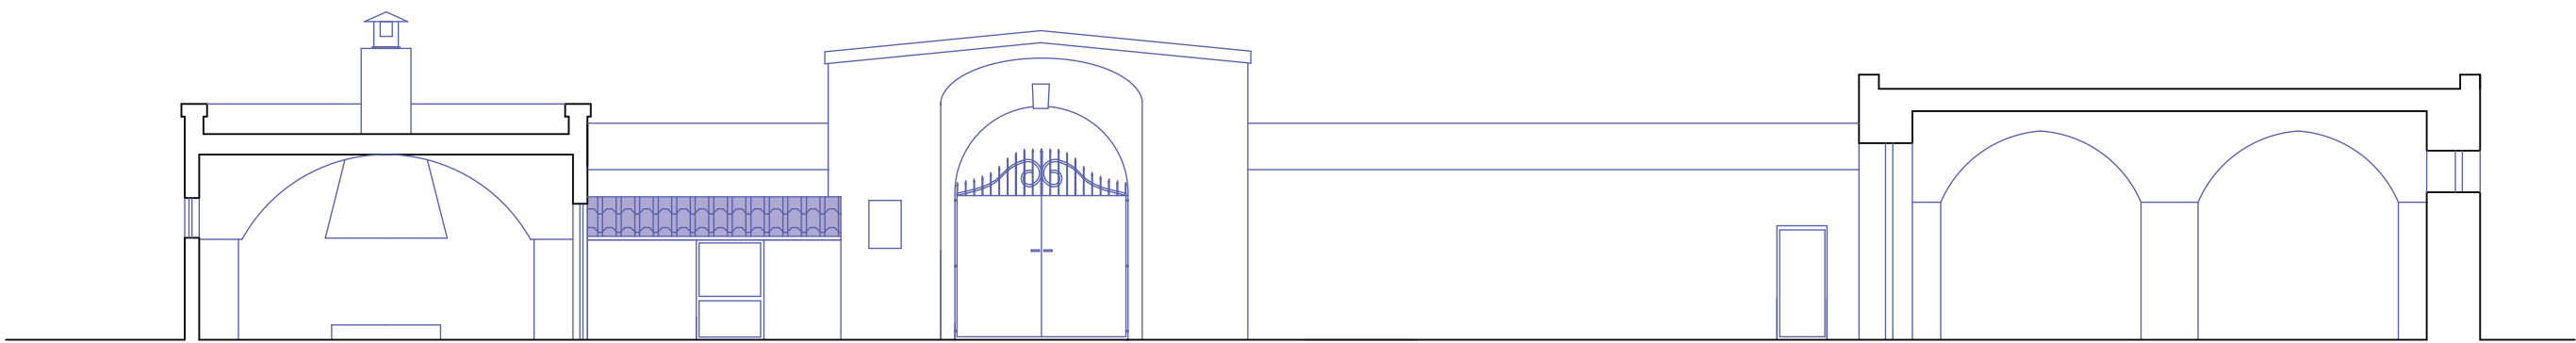


SEZIONE 1-1 VERSO ARCO D'INGRESSO -
Scala 1:100

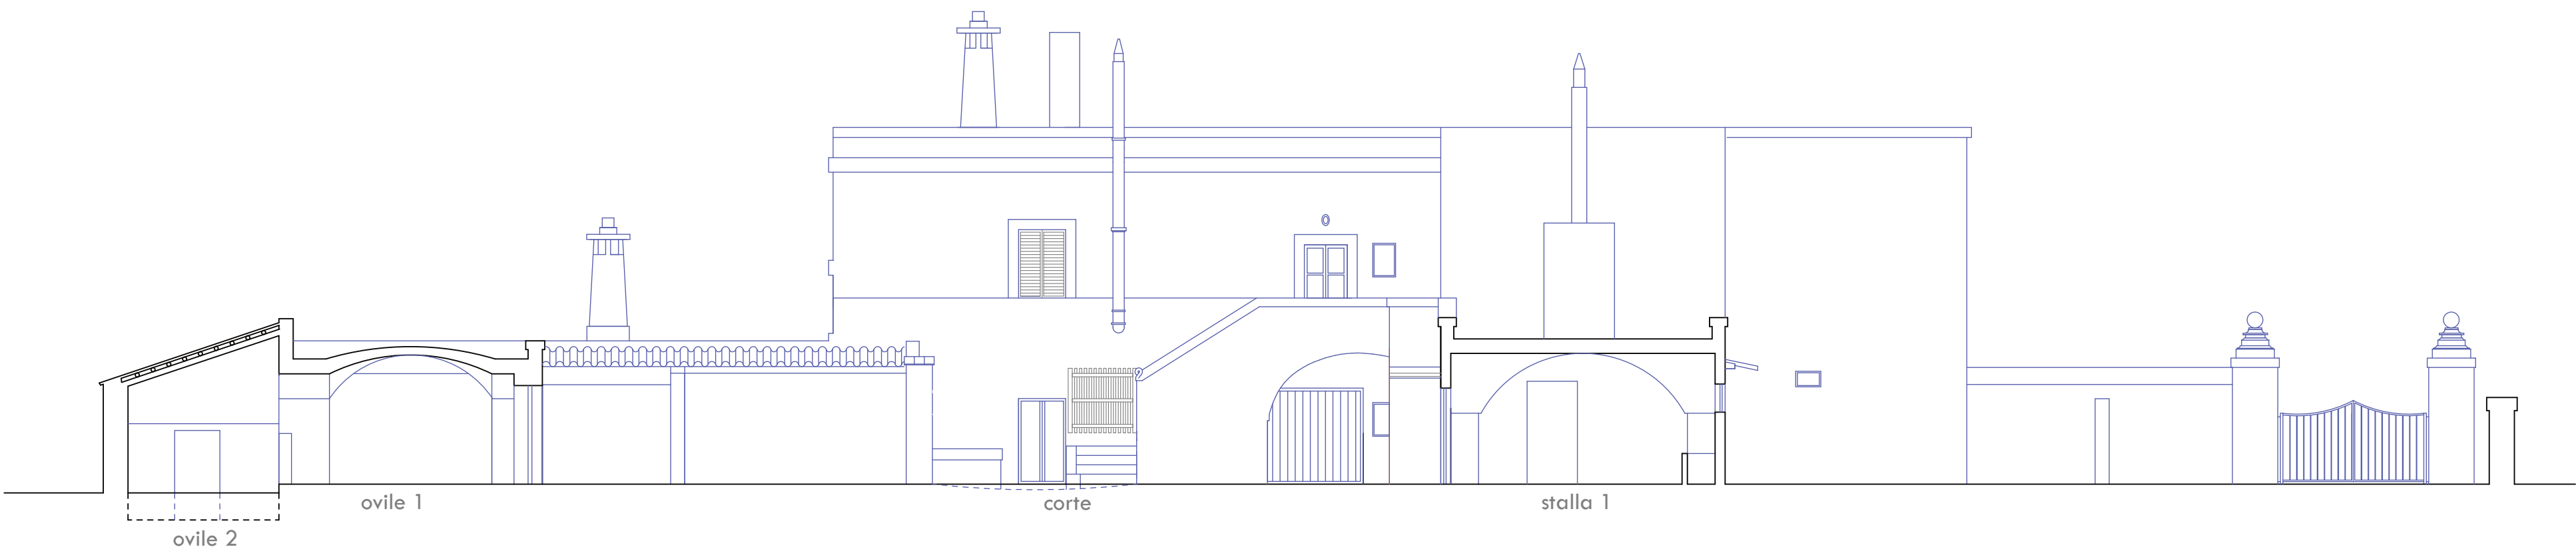

SEZIONE 2- VERSO CORPO RESIDENZIALE -
Scala 1:100

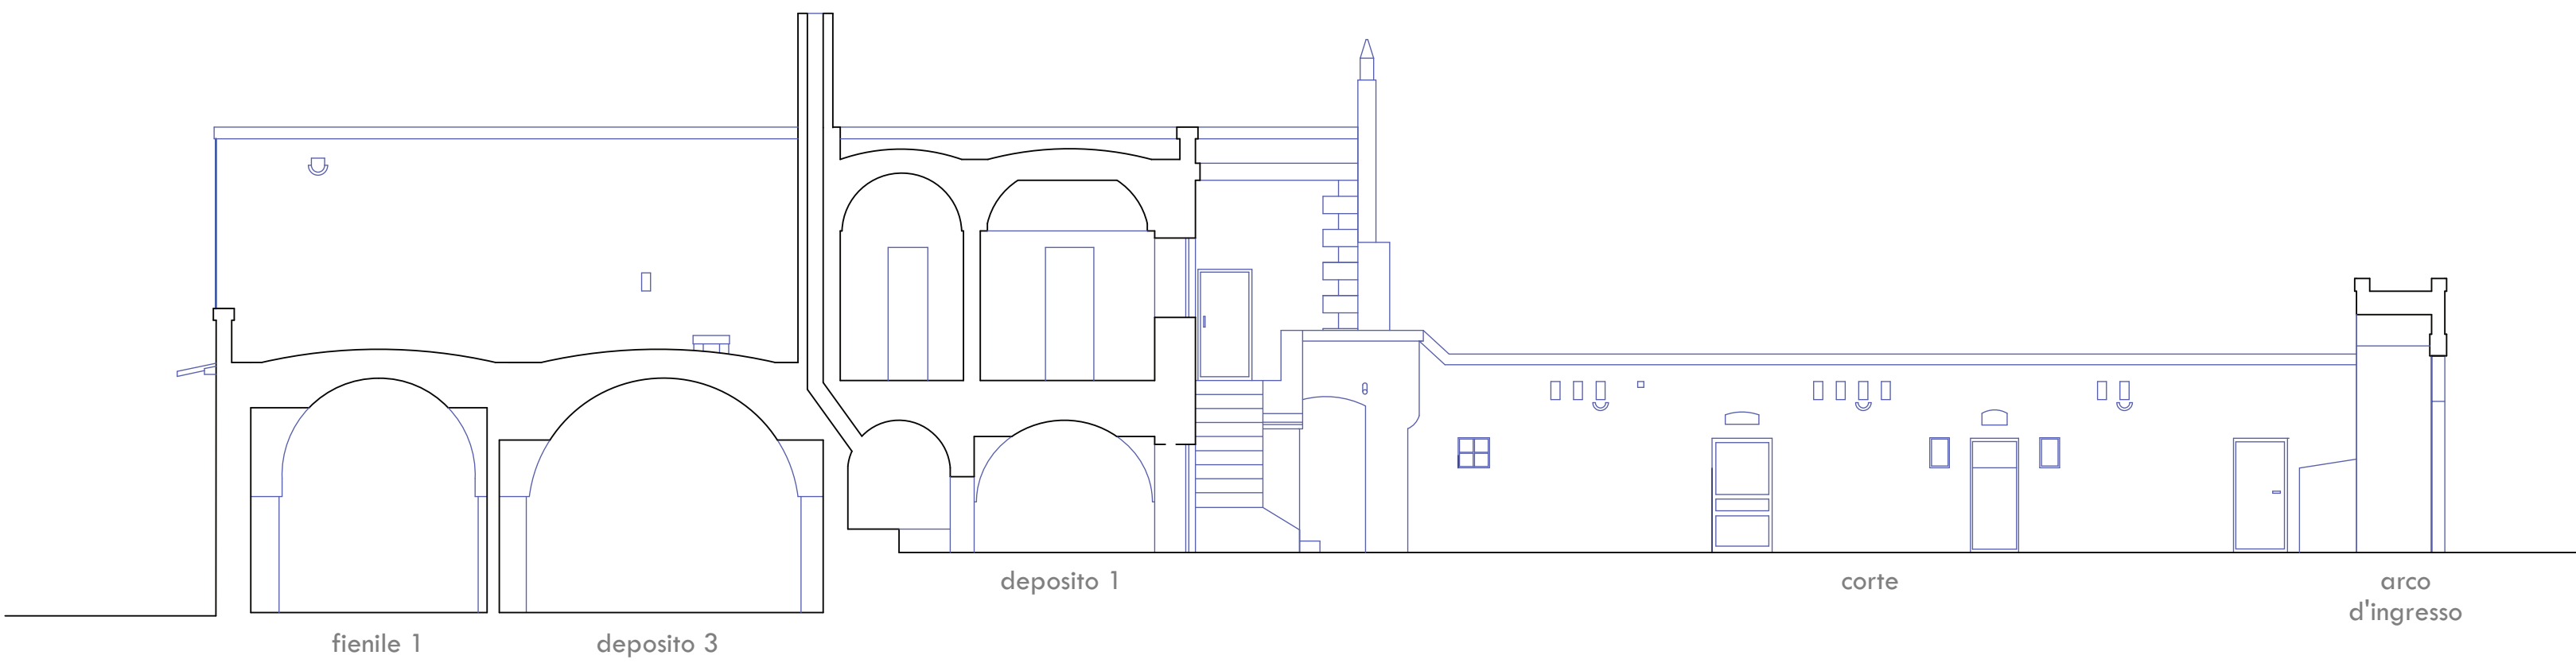

SEZIONE 3-3 VERSO STALLA BOVINI
- Scala 1:100

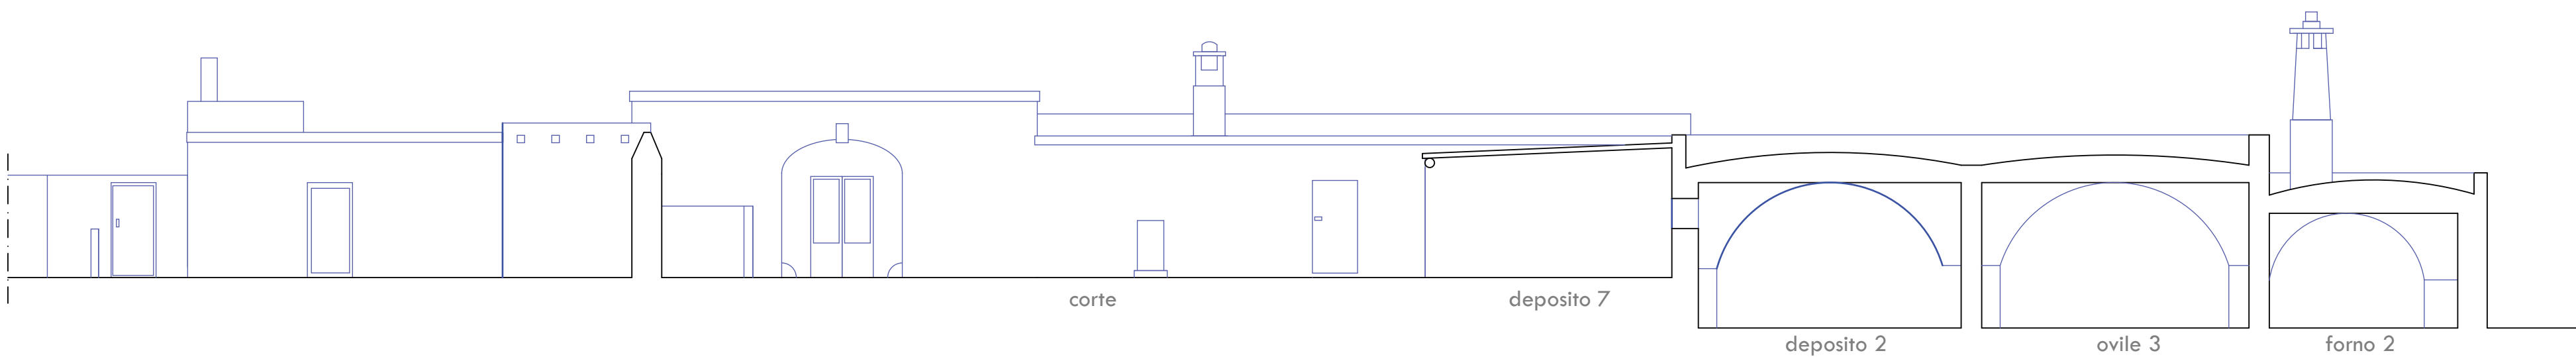

SEZIONE 4-4 VERSO STALLE CAVALLI E OVINI -
Scala 1:100

